


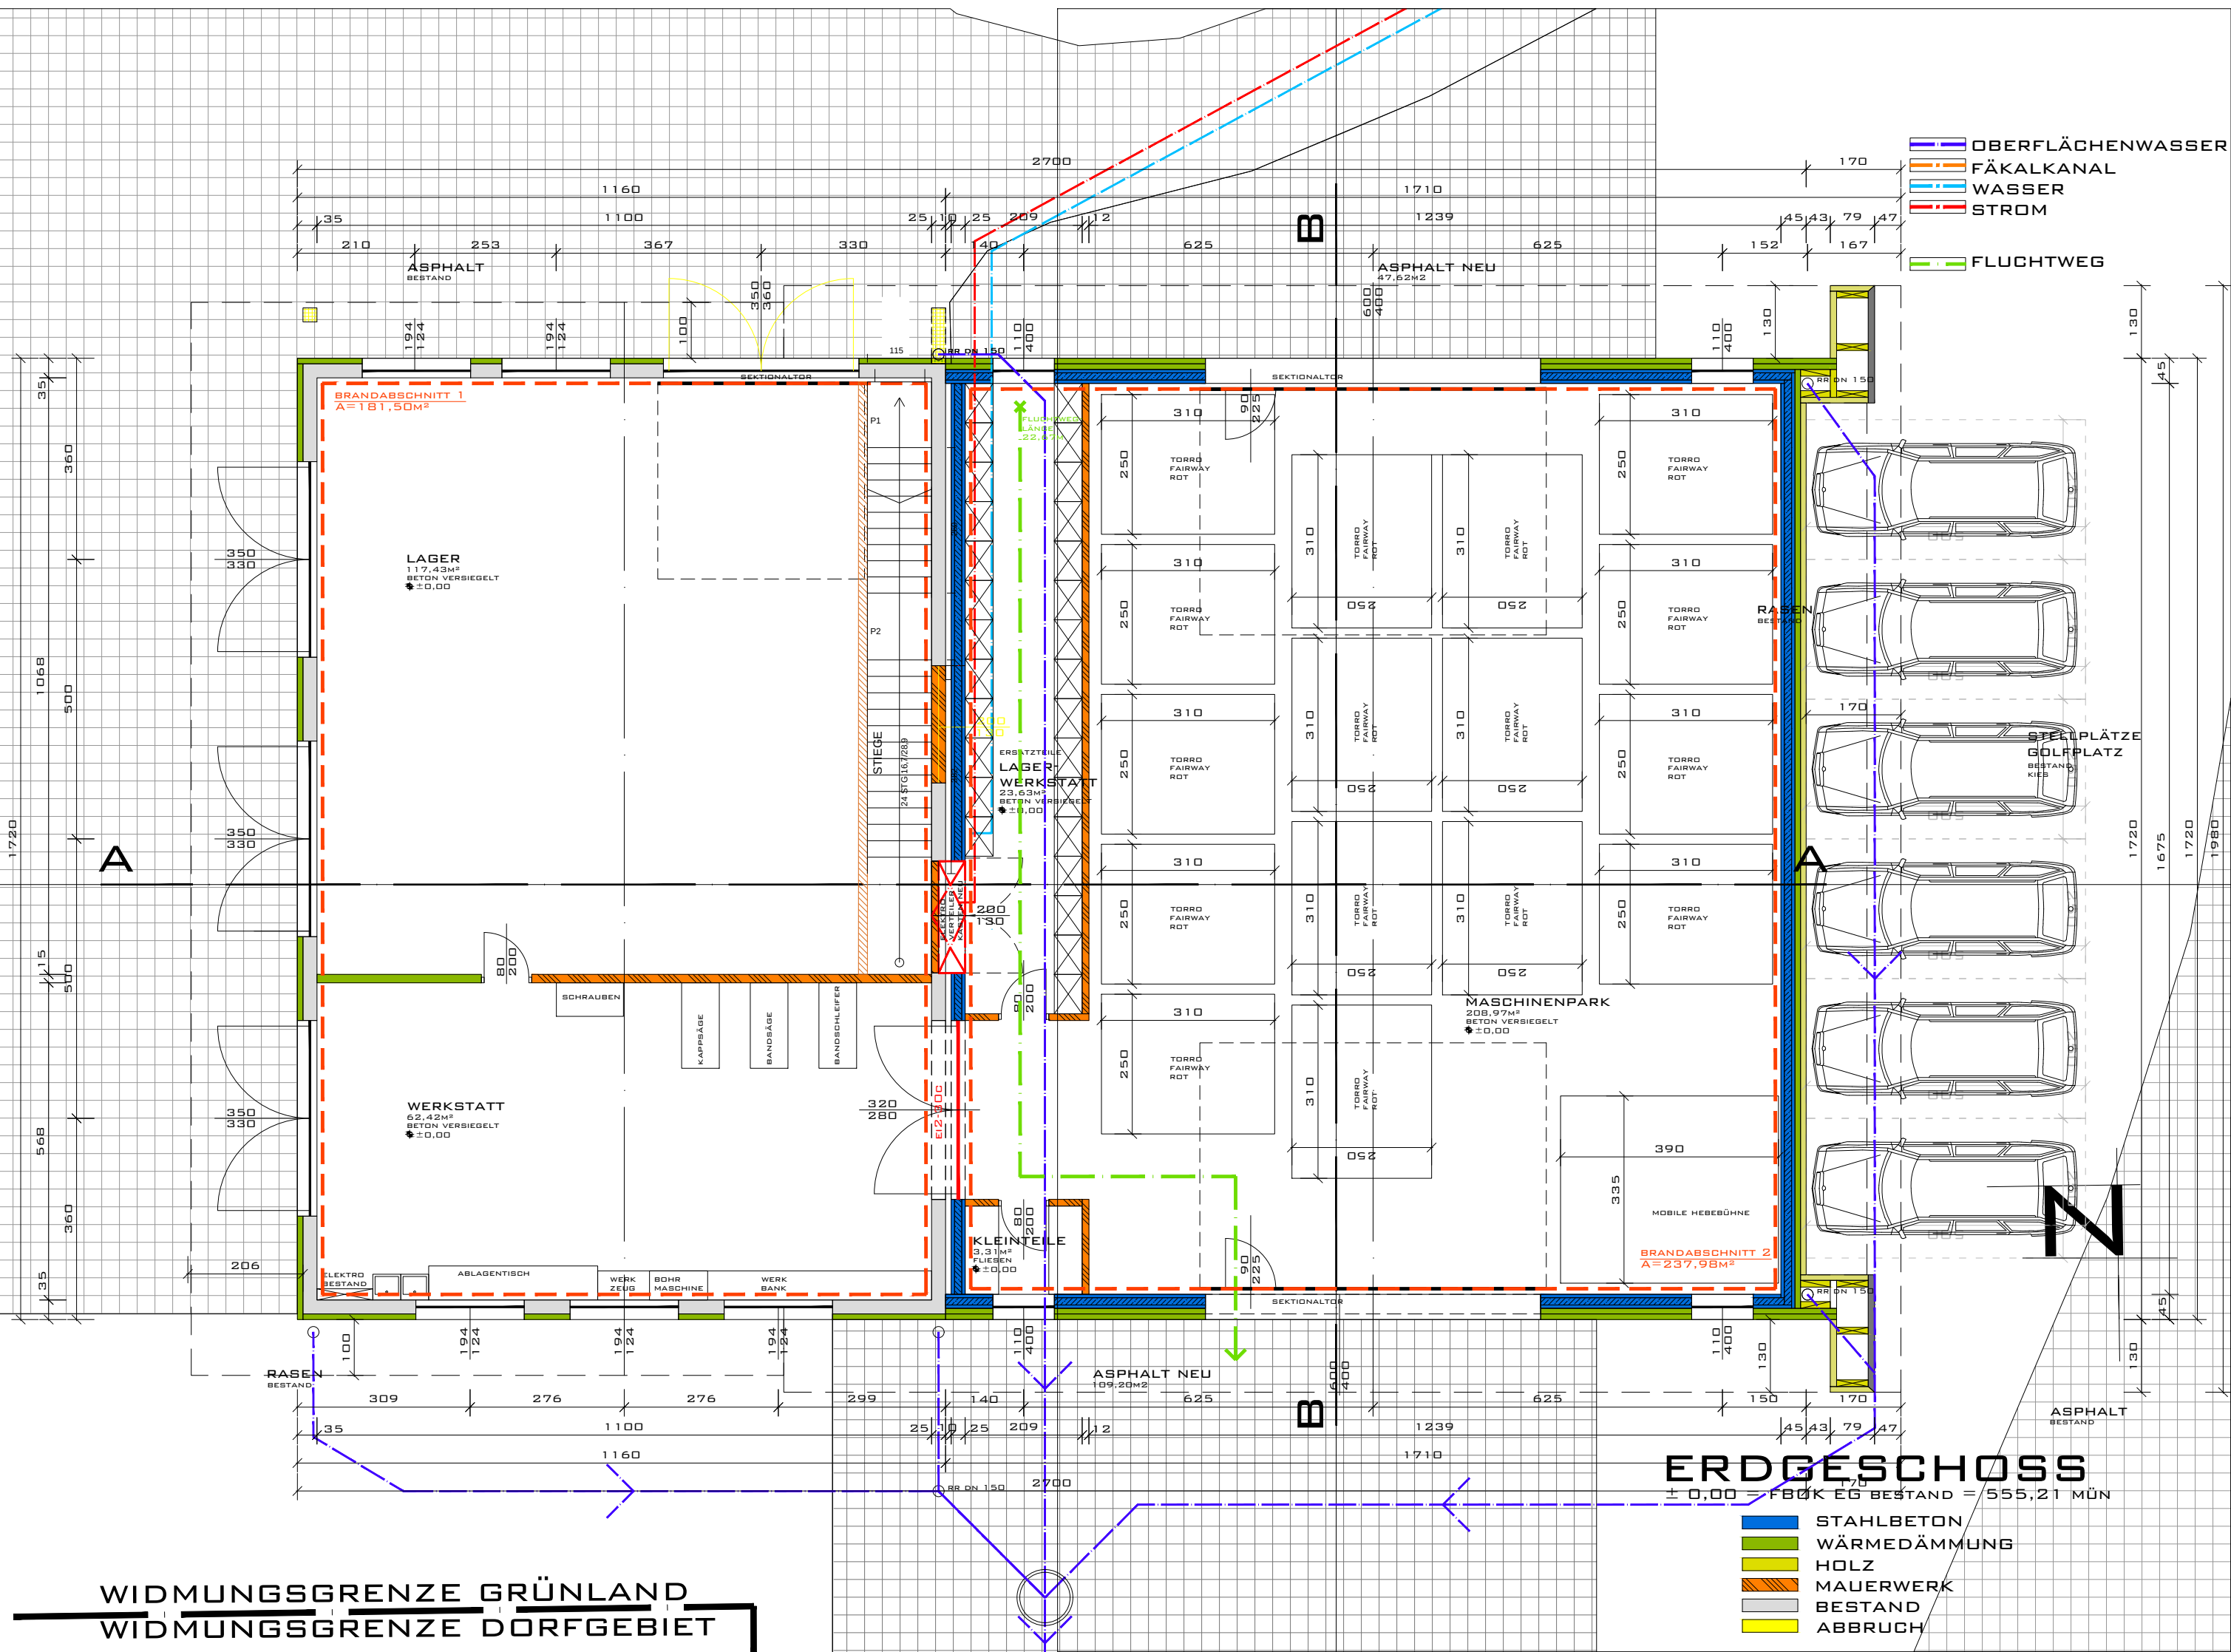

- OBERFLÄCHENWASSER
- FÄKALKANAL
- WASSER
- STROM
- FLUCHTWEG

ERDGESCHOSS

± 0,00 = FBOK EG BESTAND = 555,21 MÜN

- STAHLBETON
- WÄRMEDÄMMUNG
- HOLZ
- MAUERWERK
- BESTAND
- ABBRUCH

WIDMUNGSGRENZE GRÜNLAND
WIDMUNGSGRENZE DORFGEBIET