

EINREICHPLAN

1/100

UM- UND ZUBAU
ZUR ERRICHTUNG EINES
LANDWIRTSCHAFTLICHEN GEBÄUDES
"MASCHINENHALLE"

ST. LORENZ,
PARZELLENUMMER 1193, 1190
KG 10105 ST. LORENZ

BAUWERBER + GRUNDEIGENTÜMER

FRANZ STABAUER
AM GOLFPLATZ 1
5310 MONDSEE

BEHÖRDE:AMTLICHE VERMERKE:

BAUFÜHRER:

PLANVERFASSER:

ARCHITEKT
DIPL.- ING. DAVID HANS EBNER, PH.D.
HIERZENBERGERSTRASSE 8
5310 MONDSEE

MONDSEE AM, 26.02.2026

#2

PLANINHALT:

LAGEPLAN1/500
ERDGESCHOSS1/100
SCHNITT AA1/100
SCHNITT BB1/100
ANSICHT NORD1/100
ANSICHT OST1/100
ANSICHT SÜD1/100
ANSICHT WEST1/100

EINWENDUNGSVERZICHT

1169/1
1173
1178/3
1178/4

HANS-PETER STABAUER
KEUSCHEN 3
5310 MONDSEE

ANGELA STABAUER
KEUSCHEN 3
5310 MONDSEE

1188/3

WASSERGENOSSENSCHAFT ST. LORENZ
ST. LORENZ
5310 MONDSEE

2418/2

WASSERGENOSSENSCHAFT ST. LORENZ
ST. LORENZ
5310 MONDSEE


1178/2

MAGARETHE STABAUER
AM GOLFPLATZ 20
5310 MONDSEE

DOMINIK STABAUER
AM GOLFPLATZ 20
5310 MONDSEE

1093

CHRISTIAN FREINBERGER
THALGAUSTRASSE 40
5310 MONDSEE

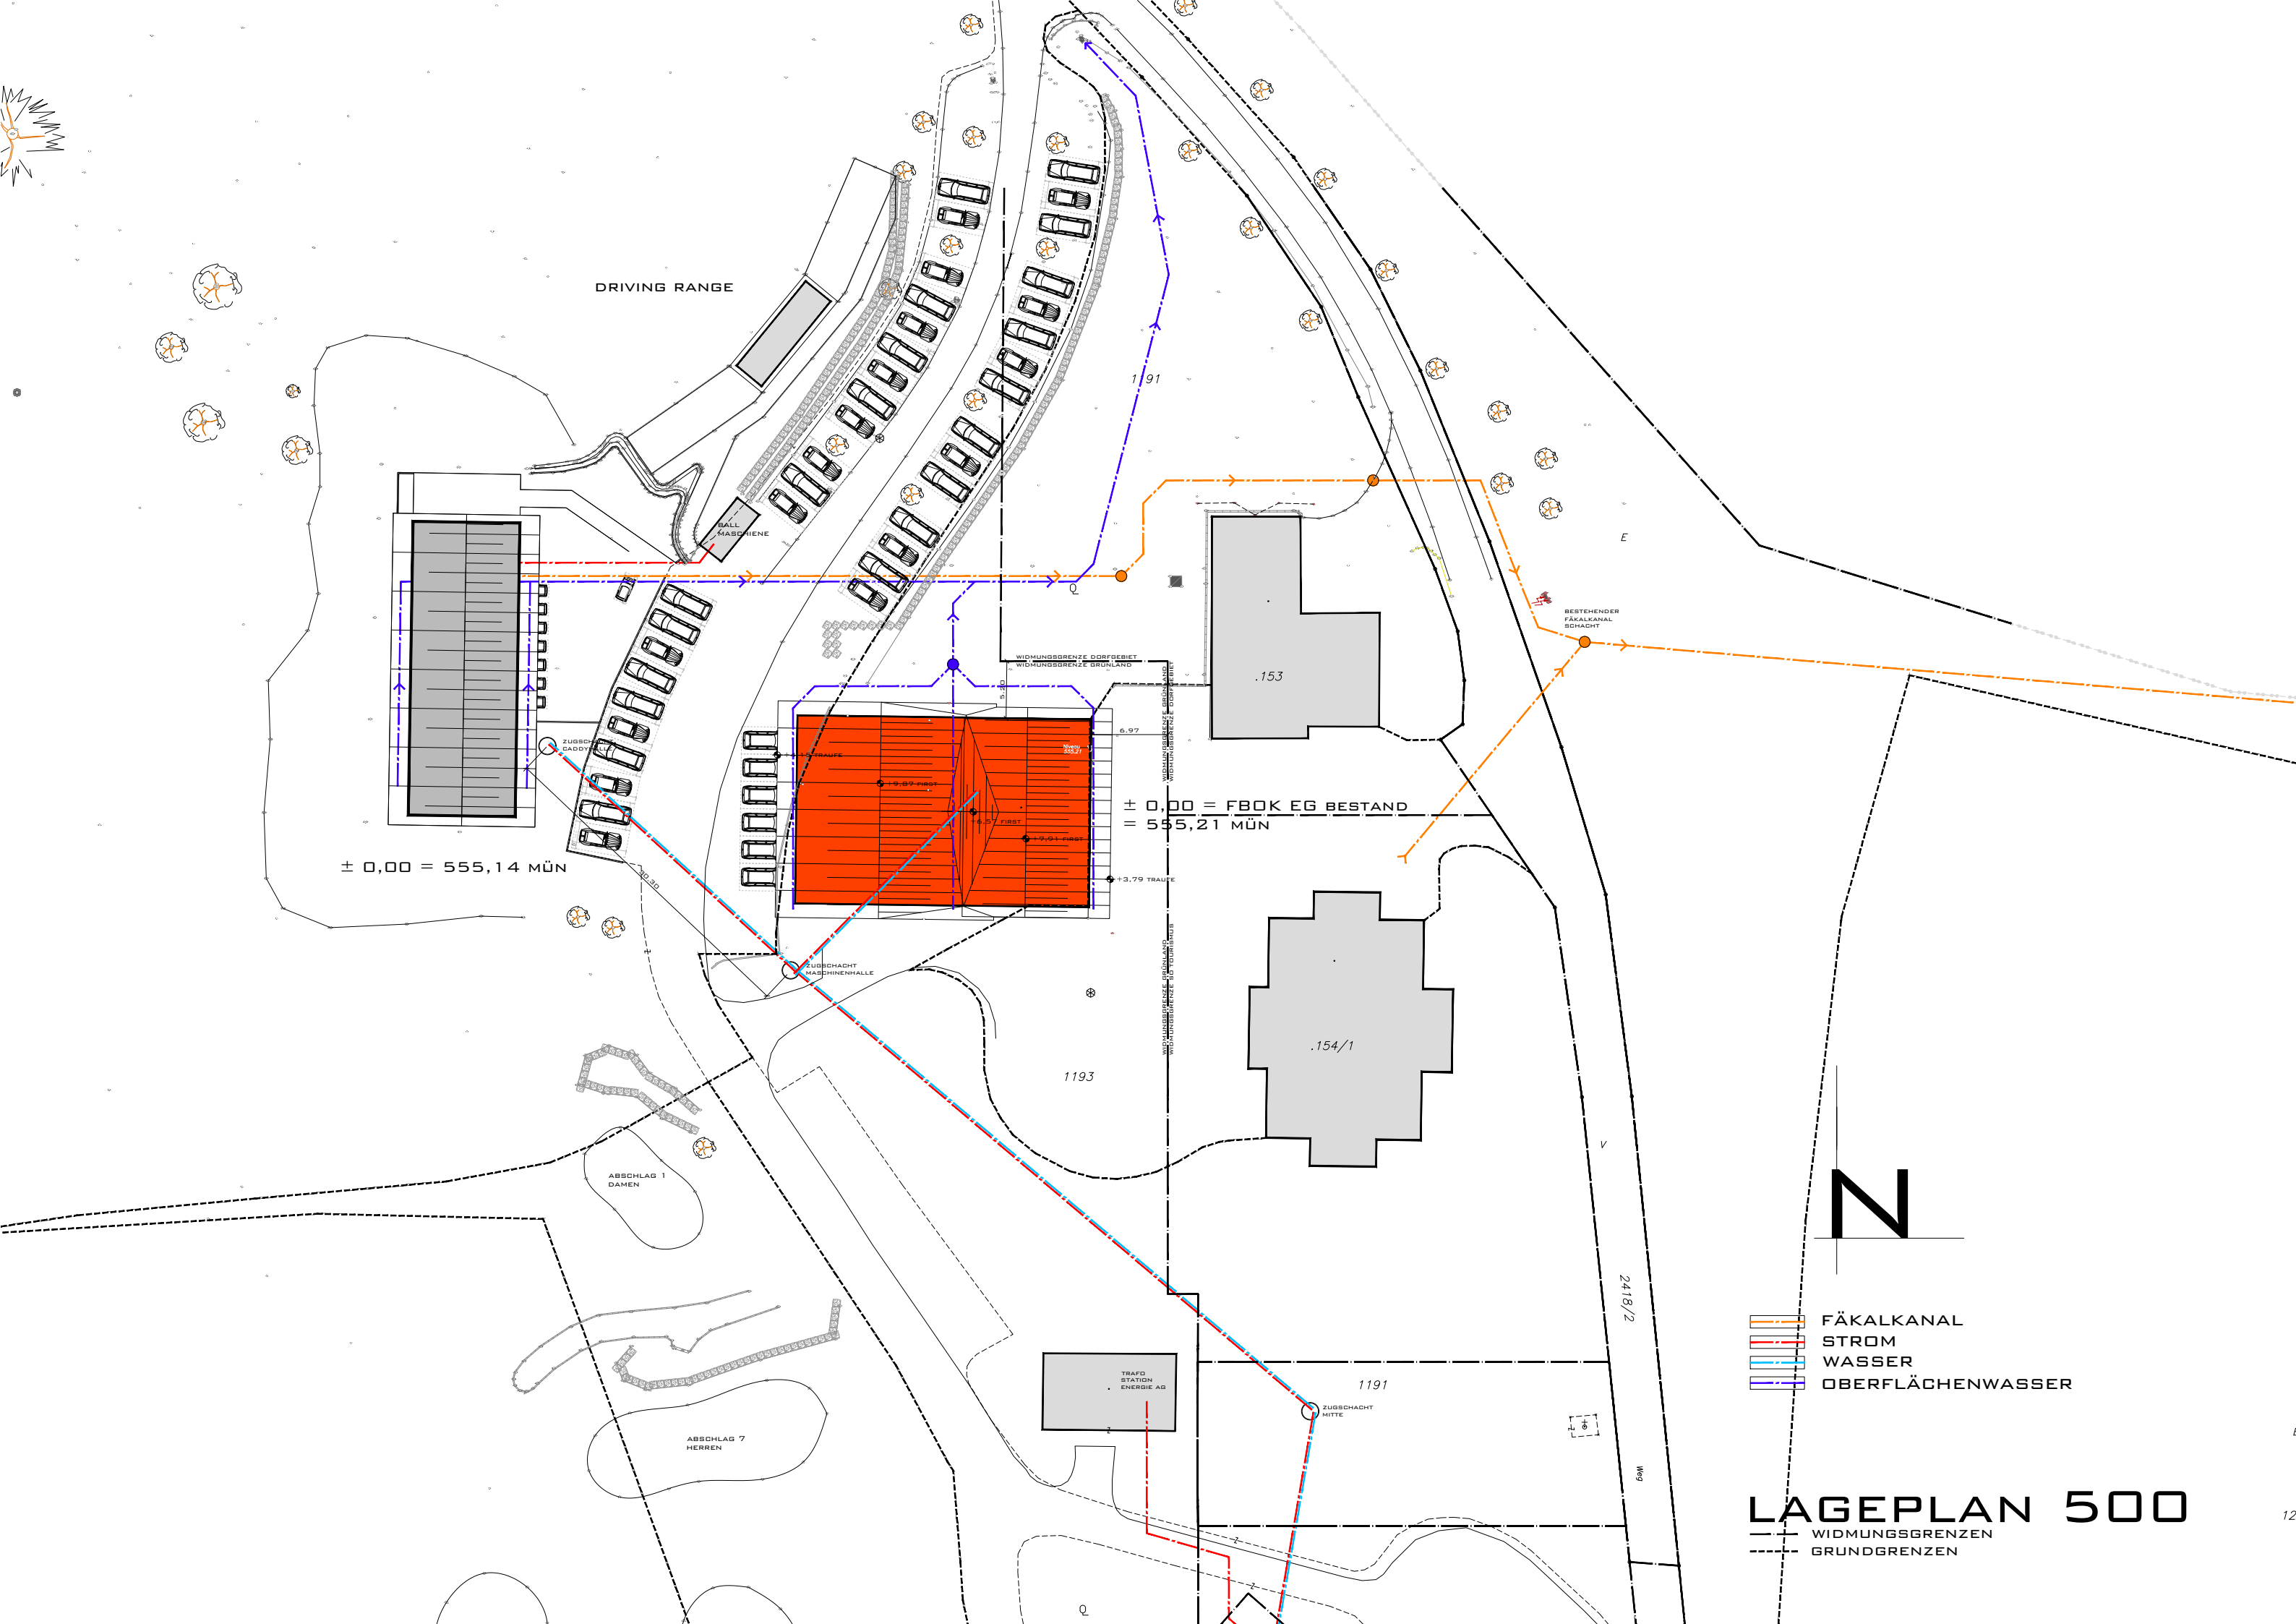

± 0,00 = 555,14 MÜN


± 0,00 = FBOK EG BESTAND
= 555,21 MÜN

N

- FÄKALKANAL
- STROM
- WASSER
- OBERFLÄCHENWASSER

LAGEPLAN 500


- WIDMUNGSGRENZEN
- GRUNDGRENZEN

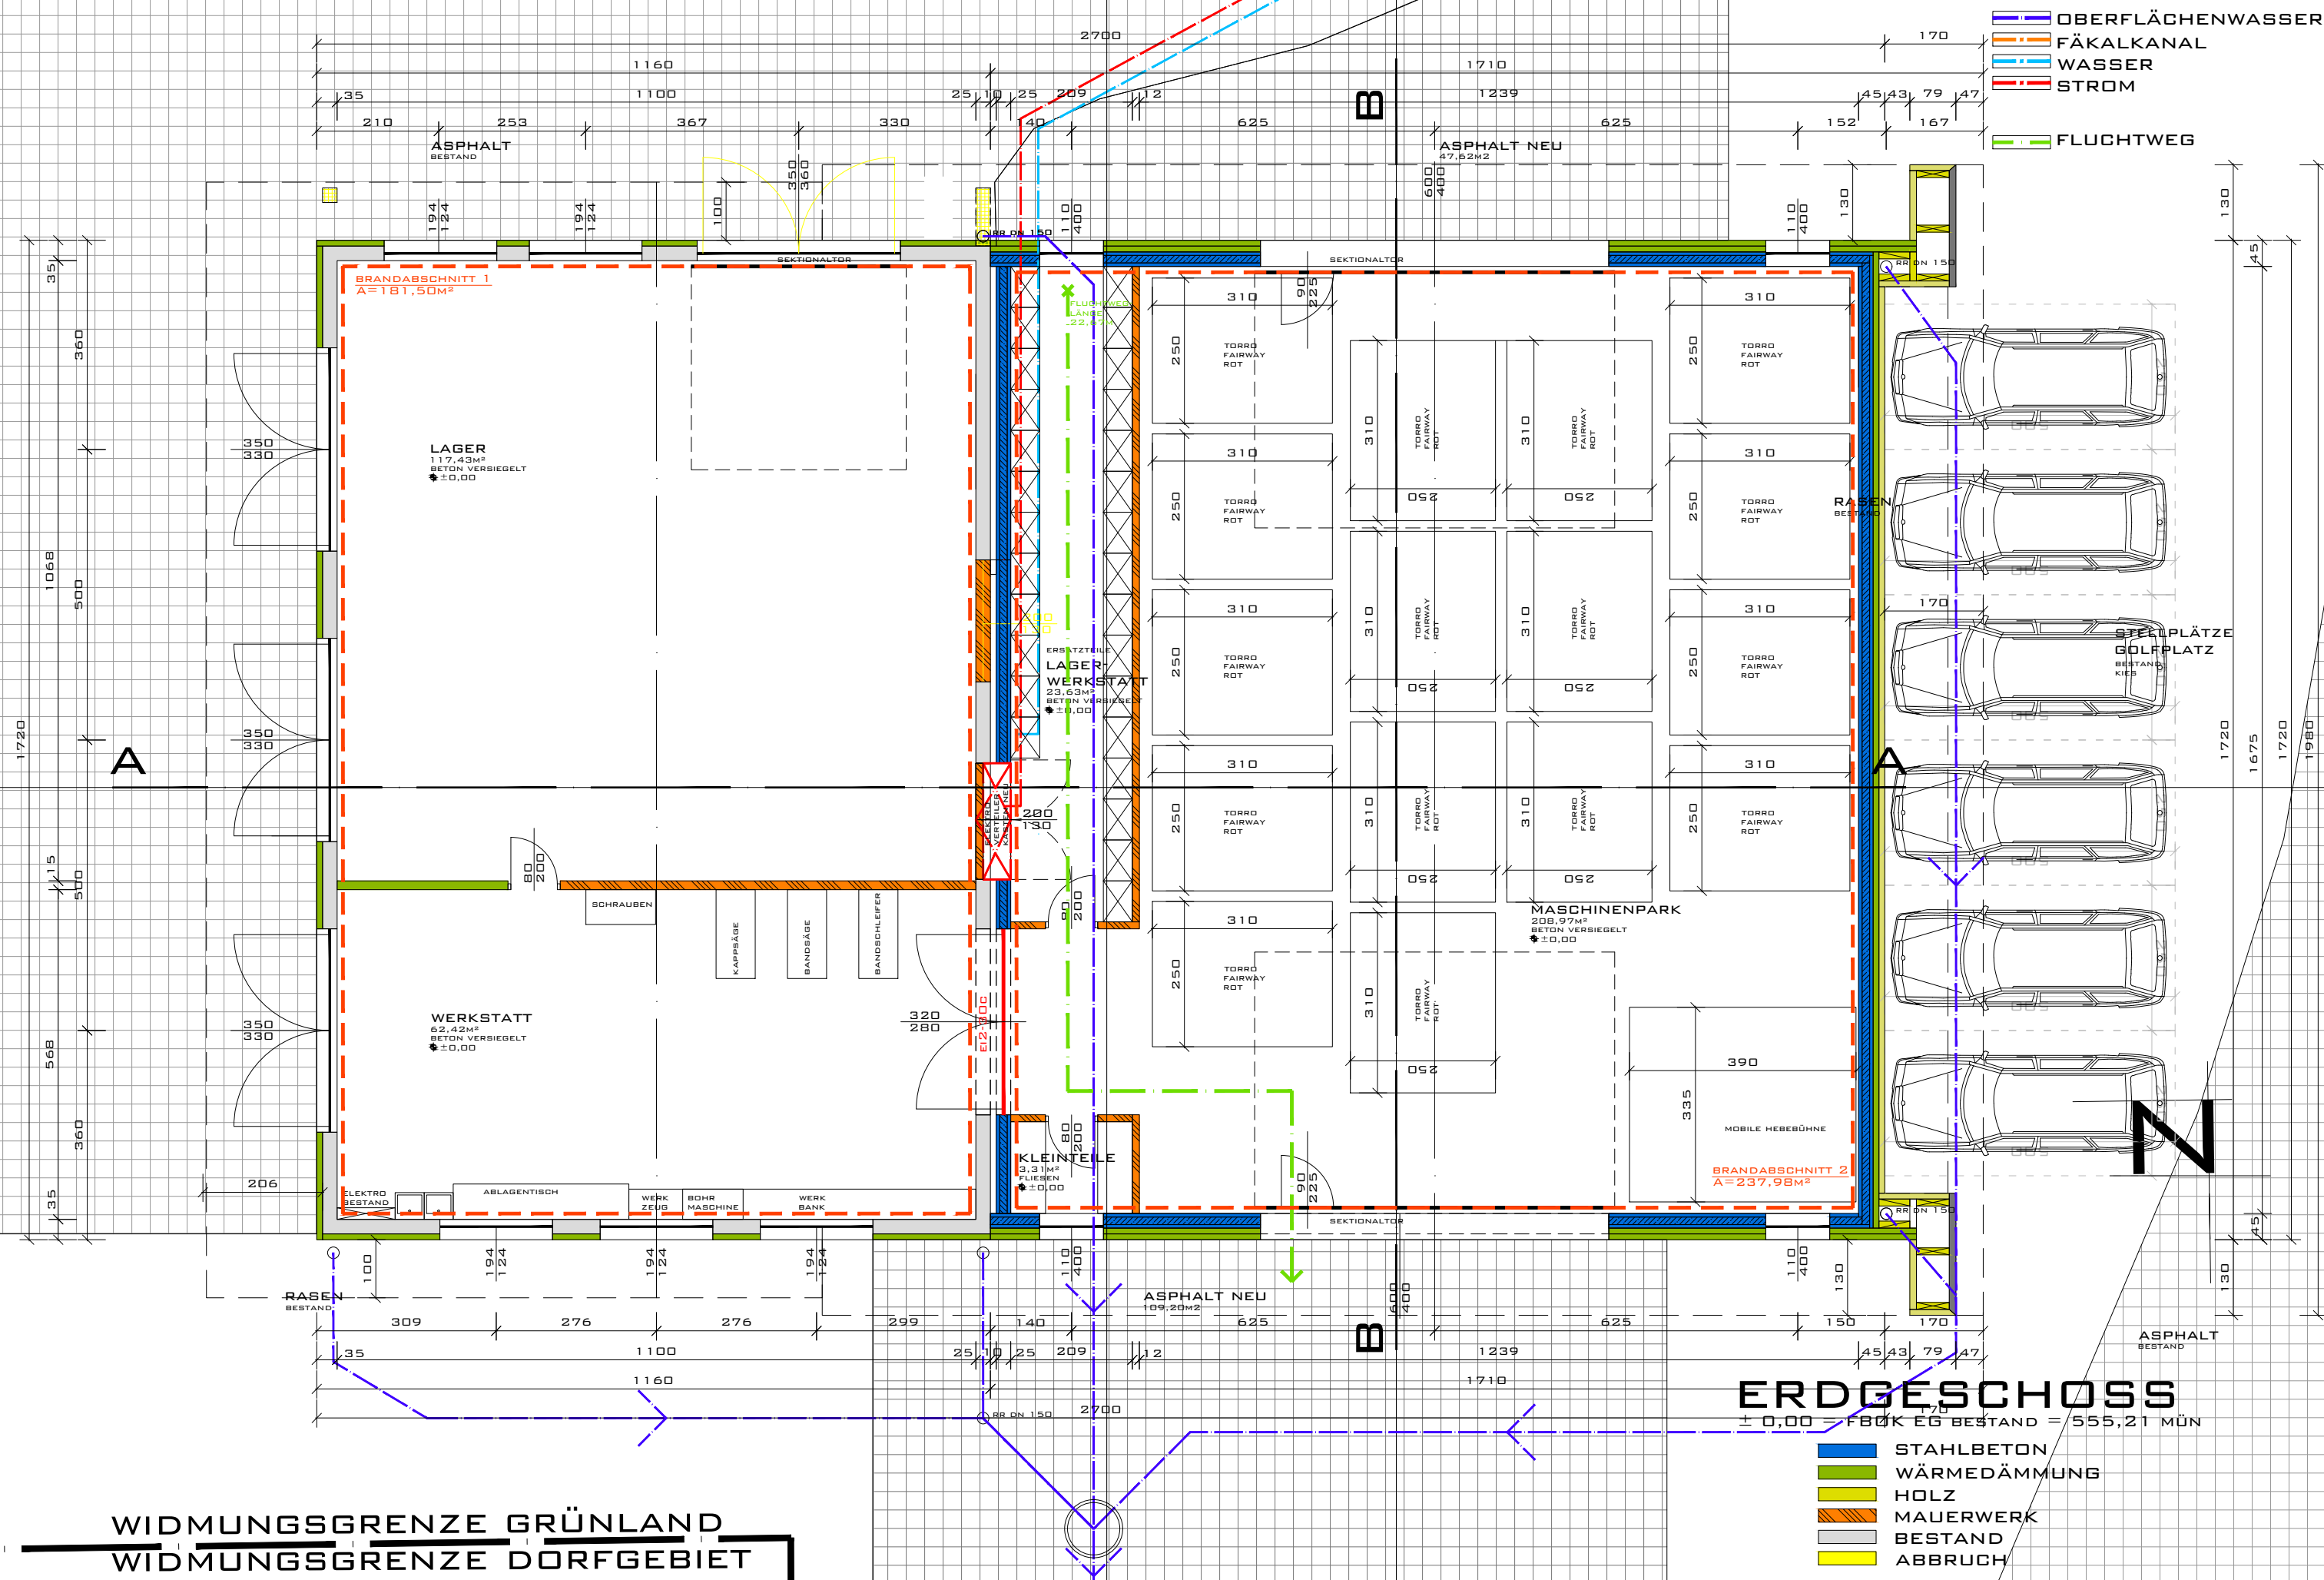

⑥	30CM	ORTBETONPLATTE LT. STATIK,
	10CM	MASCHINEL GEGLÄTTET
		SAUBERKEITSSCHICHT LT. STATIK
	30CM	2X PE- FOLIE
		BRUCHMATERIAL 32/70

5CM	DOPPELSTEHFALZDECKUNG, SCHWARZ BITUBAHN
2,4CM	DACHBAHN, VERSCHWEISST GLATTKANT BRETTER UNTERSEITE SIGHT, NUT UND FEDER
24CM	NAGELBINDER

3	5CM 2,4CM 24CM	DOPPELSTEHFALZDECKUNG, SCHWARZ DACHBAHN, VERSCHWEISST GLATTKANT BREITER UNTERSEITE SICHT, NUT UND FEDER PFETTENSPARREN
4	10CM 10CM 25CM	ALUCUBOND GOLD ELOXIERT, GEBÜRSTET AUF ALU UNTERKONSTRUKTION WÄRMEDÄMMUNG HOHLWAND, INNEN SICHT
5	10CM 25CM 1,5CM	WDVS BETONMAUERSTEIN INNENPUTZ
8	20CM 10CM 25CM	WDVS WÄRMEDÄMMUNG HOHLWAND, INNEN SICHT

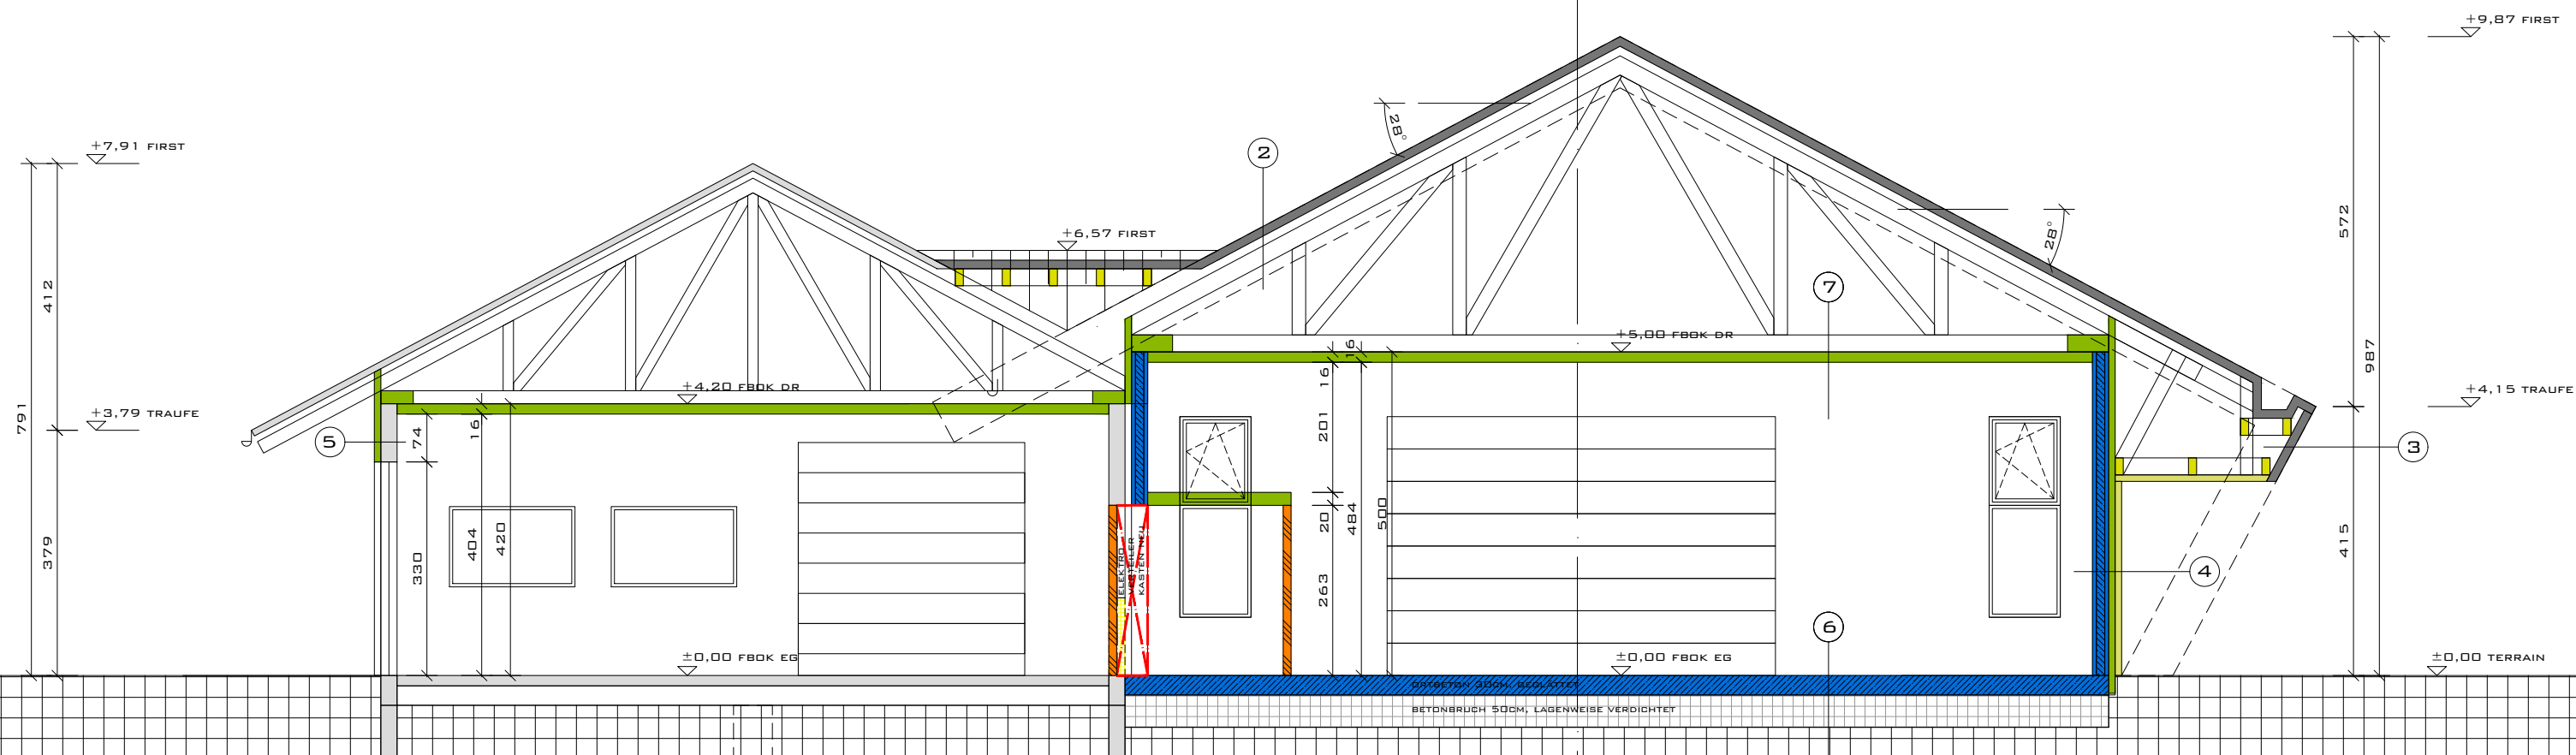

$\pm 0,00 = \text{FBOK EG BESTAND} = 555,21 \text{ MÜN}$

- | | |
|---|--------------|
|  | STAHLBETON |
|  | WÄRMEDÄMMUNG |
|  | HOLZ |
|  | MAUERWERK |
|  | BESTAND |
|  | ABBRUCH |

BODENAUFBAUTEN

- 6

30CM
10CM
30CM

ORTBETONPLATTE LT. STATIK,
MASCHINEL GEGLÄTTET
SAUBERKEITSSCHICHT LT. STATIK
2X PE- FOLIE
BRUCHMATERIAL 32/70
- 7

24CM
16CM

NAGELBINDER
PU SANDWICHPANEEL

DACHAUFBAUTEN

- 2

5CM
2,4CM
24CM

DOPPELSTEHFALZDECKUNG, SCHWARZ
BITUBAHN
DACHBAHN, VERSCHWEISST
GLATTKANT BRETTER UNTERSEITE SICHT,
NUT UND FEDER
NAGELBINDER

WANDAUFBAUTEN

- 3

5CM
2,4CM
24CM

DOPPELSTEHFALZDECKUNG, SCHWARZ
DACHBAHN, VERSCHWEISST
GLATTKANT BRETTER UNTERSEITE SICHT,
NUT UND FEDER
PFETTENSPARREN
- 4

10CM
10CM
25CM




ALUCUBOND GOLD ELOXIERT, GEBÜRSTET
AUF ALU UNTERKONSTRUKTION
WÄRMEDÄMMUNG
HOHLWAND, INNEN SICHT
- 5

10CM
25CM
1,5CM

WDVS
BETONMAUERSTEIN
INNENPUTZ
- 8

20CM
10CM
25CM


WDVS
WÄRMEDÄMMUNG
HOHLWAND, INNEN SICHT

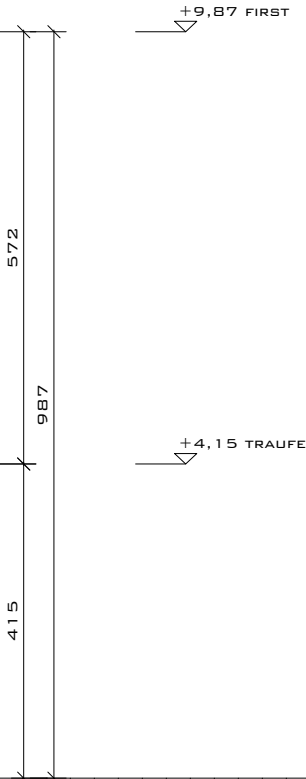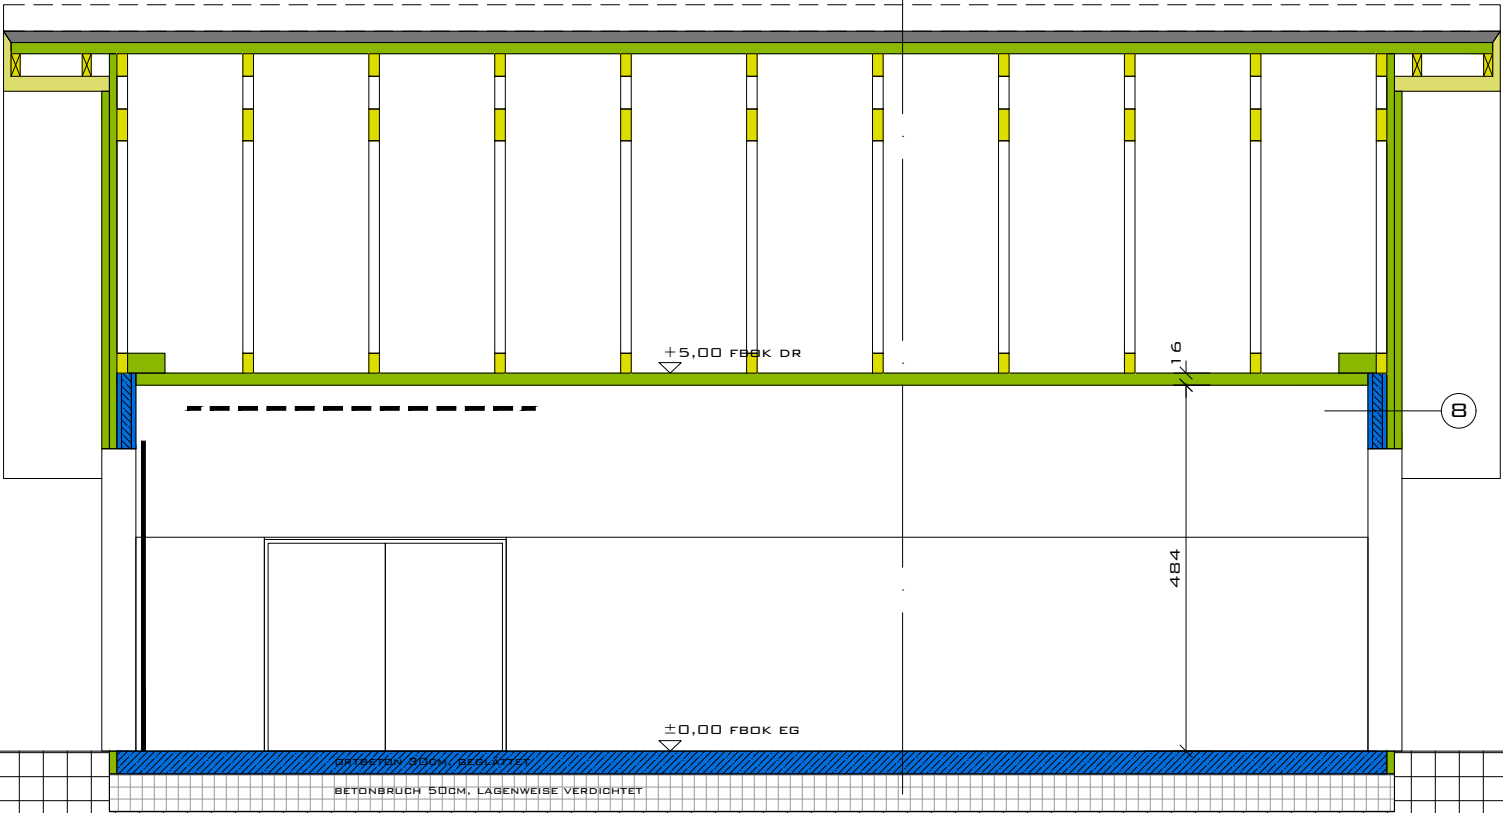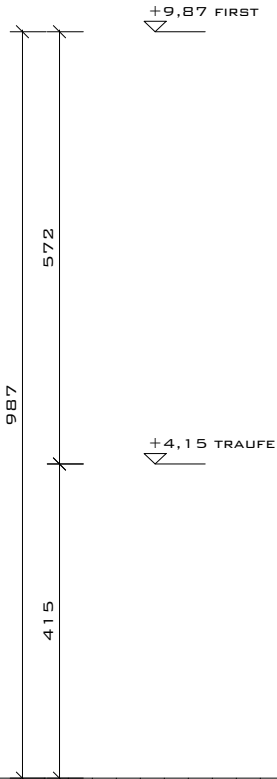

SCHNITT BB

± 0,00 = FBOK EG BESTAND = 555,21 MÜN

- STAHLBETON
- WÄRMEDÄMMUNG
- HOLZ
- MAUERWERK
- BESTAND
- ABBRUCH



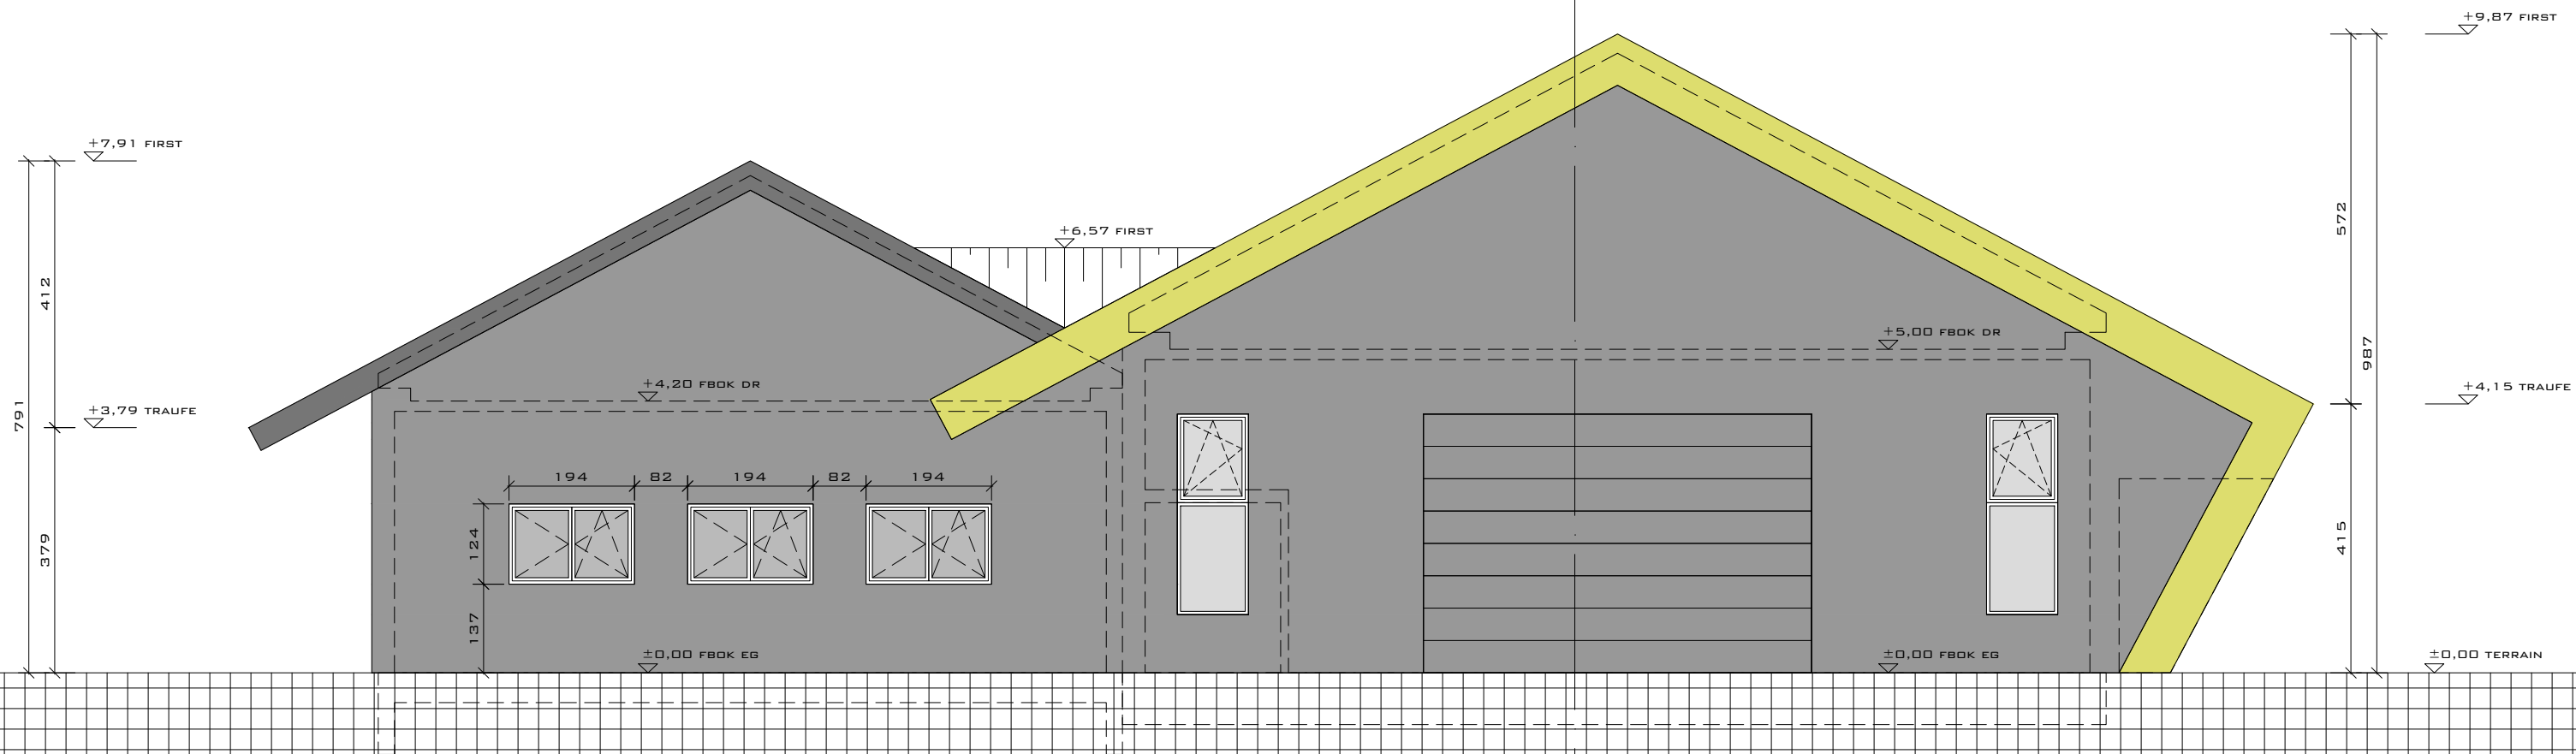


ANSICHT NORD

± 0,00 = FBOK EG BESTAND = 555,21 MÜN

- STAHLBETON
- WÄRMEDÄMMUNG
- HOLZ
- MAUERWERK
- BESTAND
- ABBRUCH


A

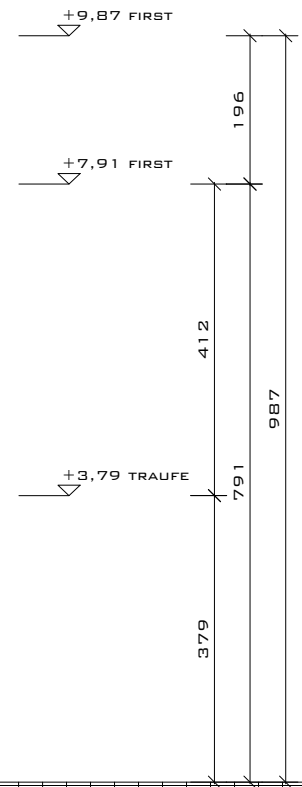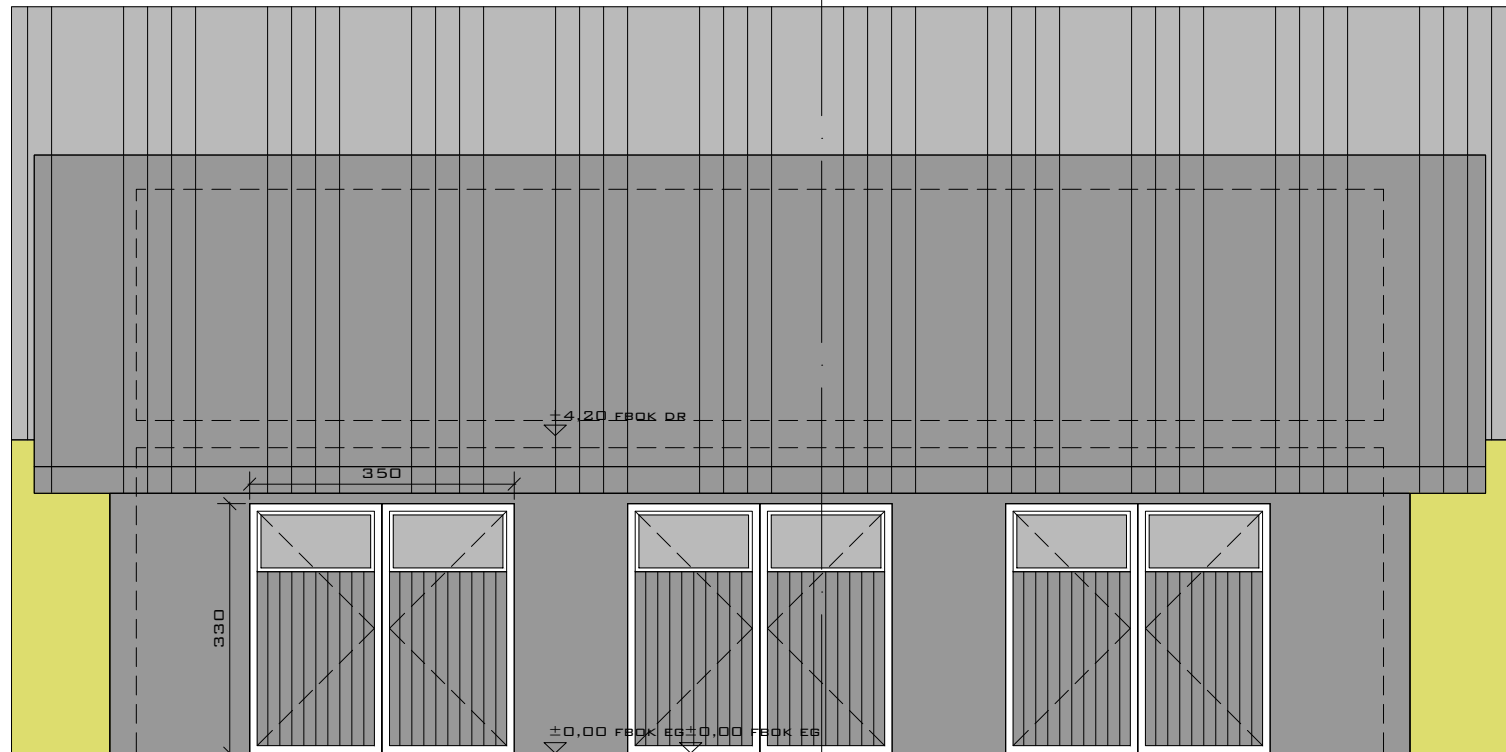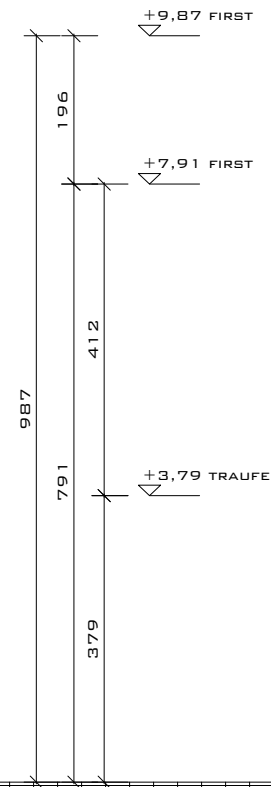

ANSICHT OST
± 0,00 = FBOK EG BESTAND = 555,21 MÜN

■	STAHLBETON
■	WÄRMEDÄMMUNG
■	HOLZ
■	MAUERWERK
■	BESTAND
■	ABBRUCH

A

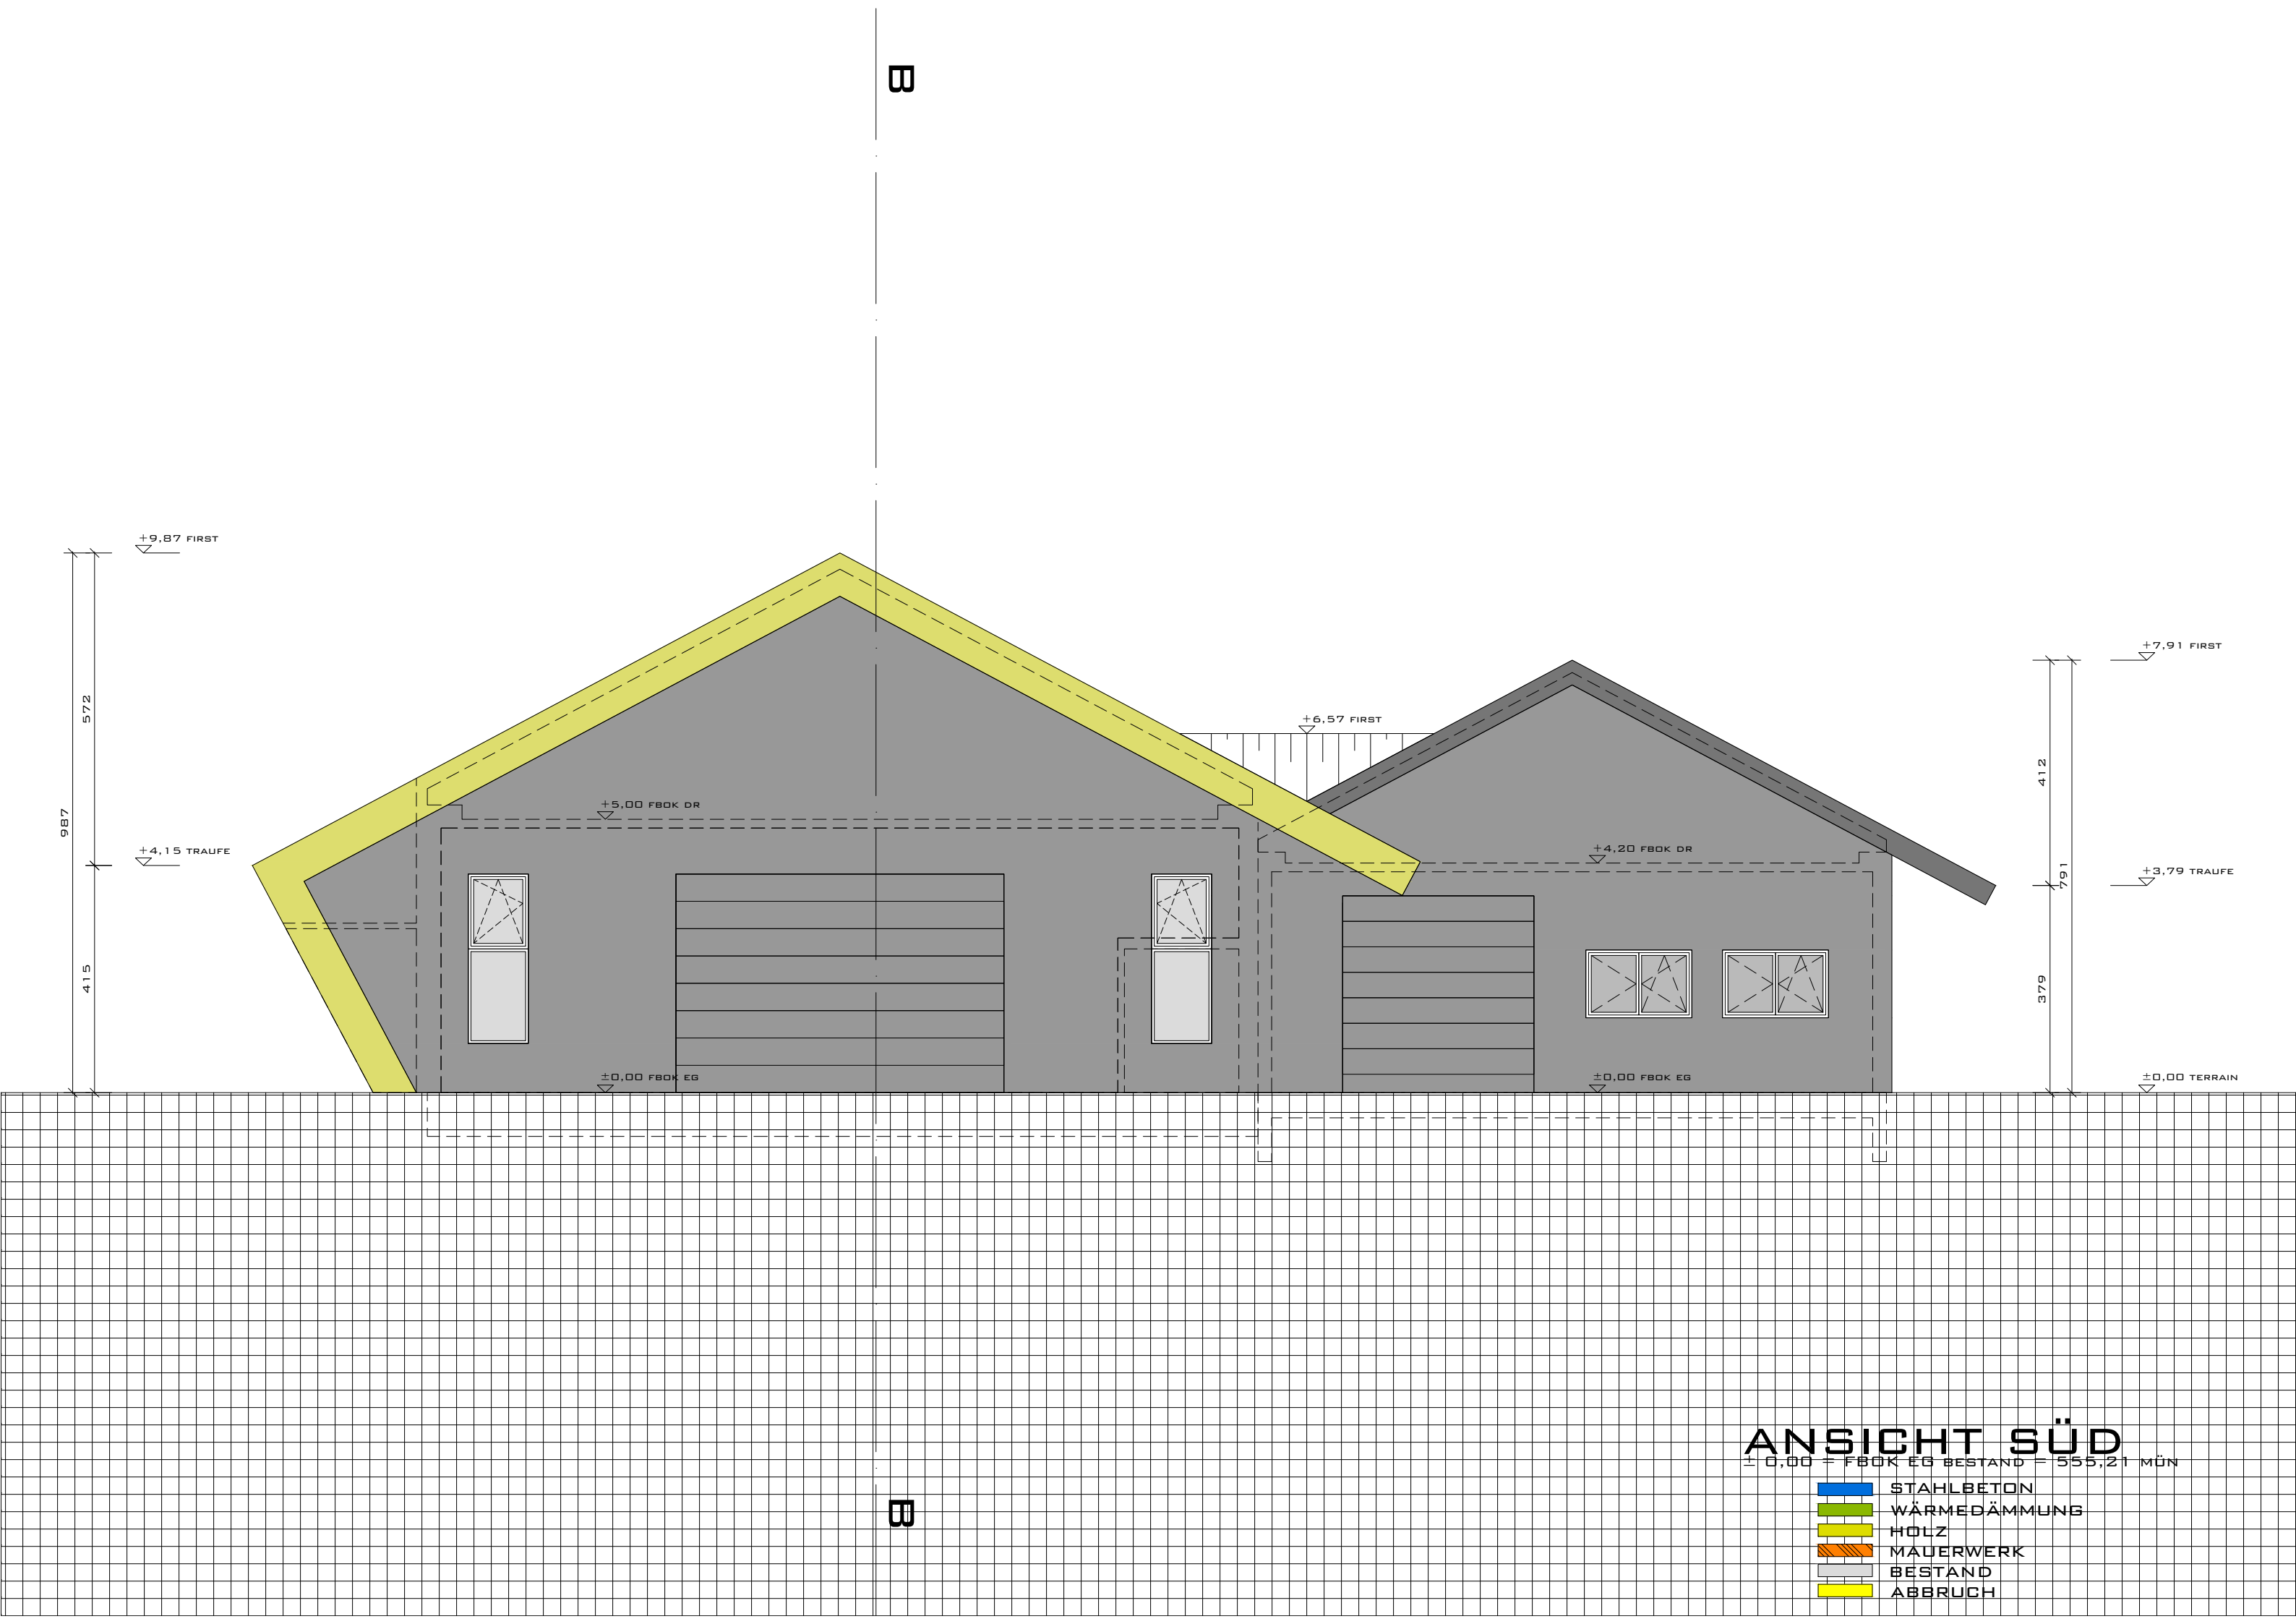




S

S

ANSICHT SÜD

± 0,00 = FBOK EG BESTAND = 555,21 MÜN

- STAHLBETON
- WÄRMEDÄMMUNG
- HOLZ
- MAUERWERK
- BESTAND
- ABBRUCH

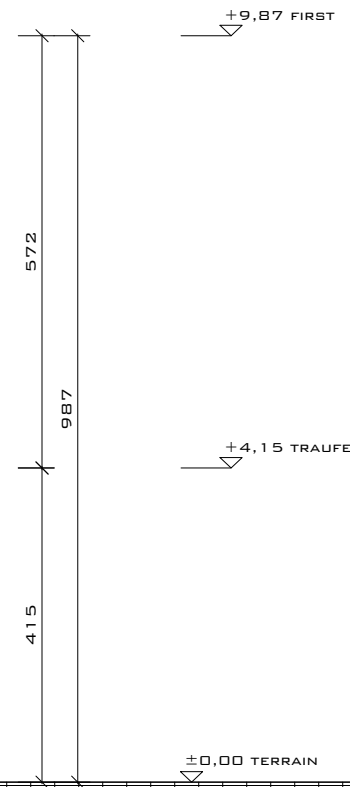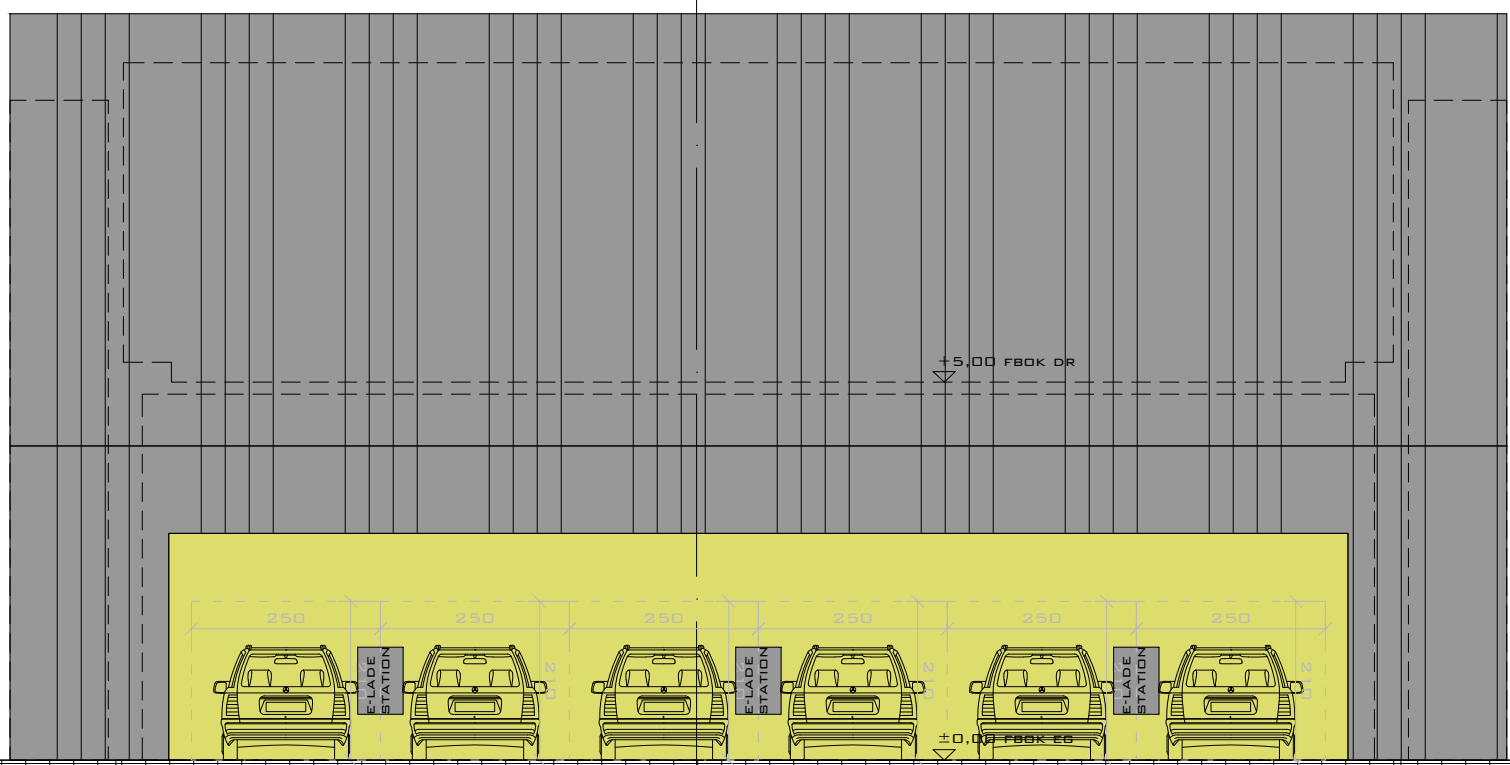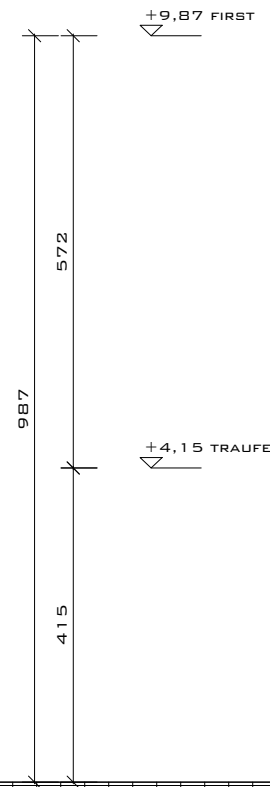

ANSICHT WEST

± 0,00 = F80K EG BESTAND = 555,21 MÜN

■	STAHLBETON
■	WÄRMEDÄMMUNG
■	HOLZ
■	MAUERWERK
■	BESTAND
■	ABBRUCH